



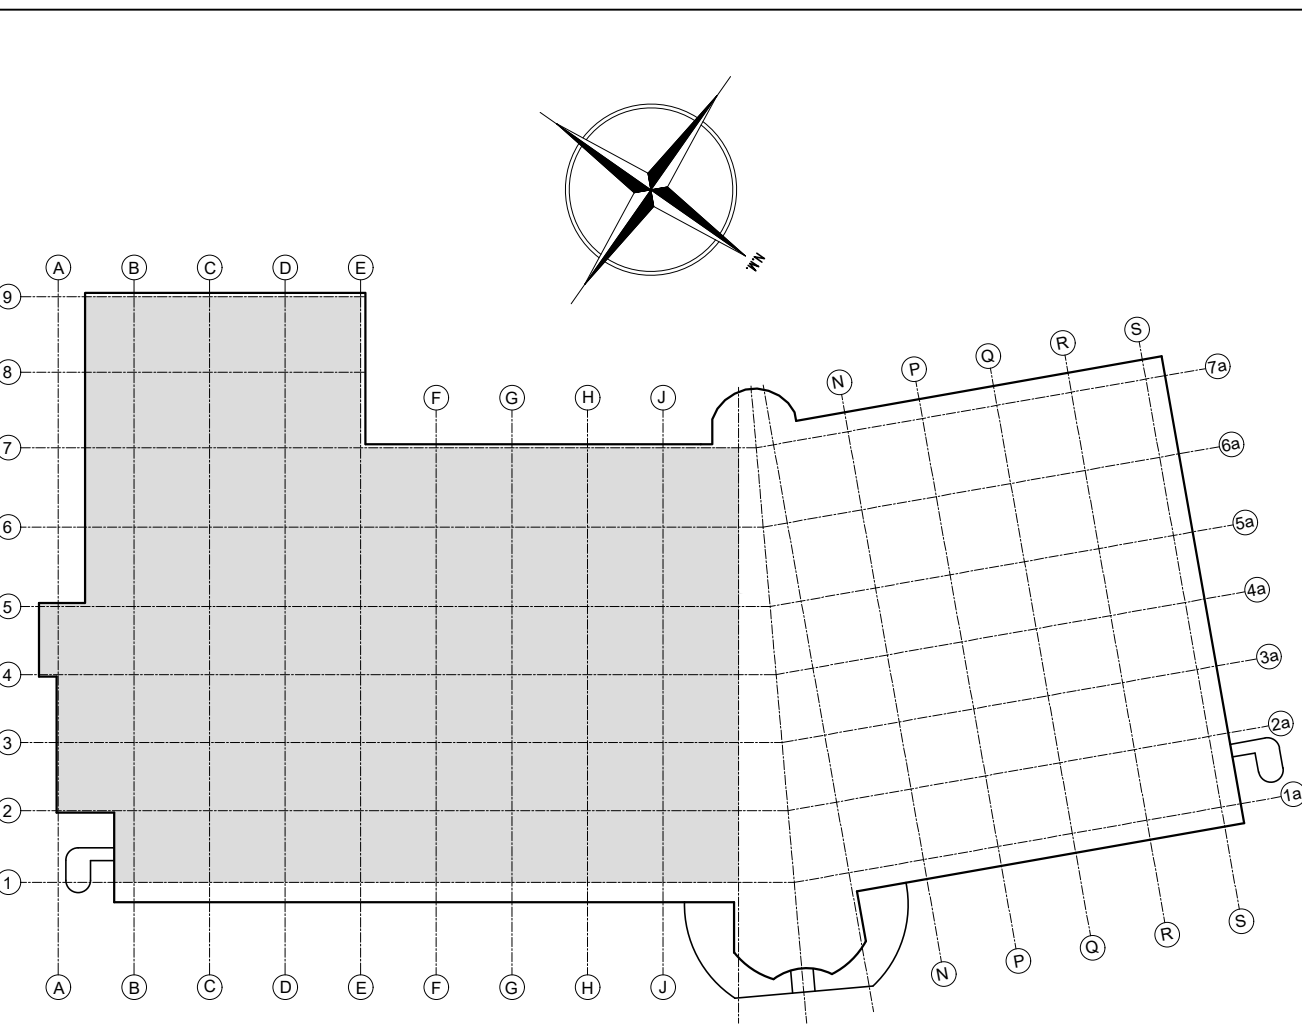

FLUXO DE APROVAÇÃO APPROVAL FLOW		
EMISSOR ISSUER	REVISOR REVIEWER	APROVAÇÃO APPROVAL
Nome: _____	Nome: _____	Nome: _____
Área: _____	Área: _____	Área: _____
DATA: ____/____/____	DATA: ____/____/____	DATA: ____/____/____

09	CM783-DEDUÇÃO DA FASE 019 DO LABORATÓRIO 02	09/2023	EQ.ENG.*
08	CM783-DEDUÇÃO DA FASE 019 DO LABORATÓRIO 02	03/2023	EQ.ENG.*
07	CM7394-Fase 1 - MasterPlan 02	01/2023	EQ.ENG.*
06	CM7136-Equipamento-Absorção Atômica	09/2022	EQ.ENG.*
05	CM5659-Equipamento-Lab.Filtração	08/2022	EQ.ENG.*
04	ERU22225-P22018 SALA DE REUNIÃO 00	11/2021	EQ.ENG.*
03	Atualização dos nomes dos solos dos laboratórios	01/2018	EQ.ENG.*
02	ERU2111-P21036 ADEQ.SALA MEDIA FILL	05/2017	EQ.ENG.*
01	P/ CADASTRAMENTO NO SEVISA	02/2017	EQ.ENG.*
00	LAYOUT DE ESCRITÓRIO - TAG022	06/2016	EQ.ENG.*
REV	DESCRIÇÃO	DATA	APROV.

LOGO PROJETISTA

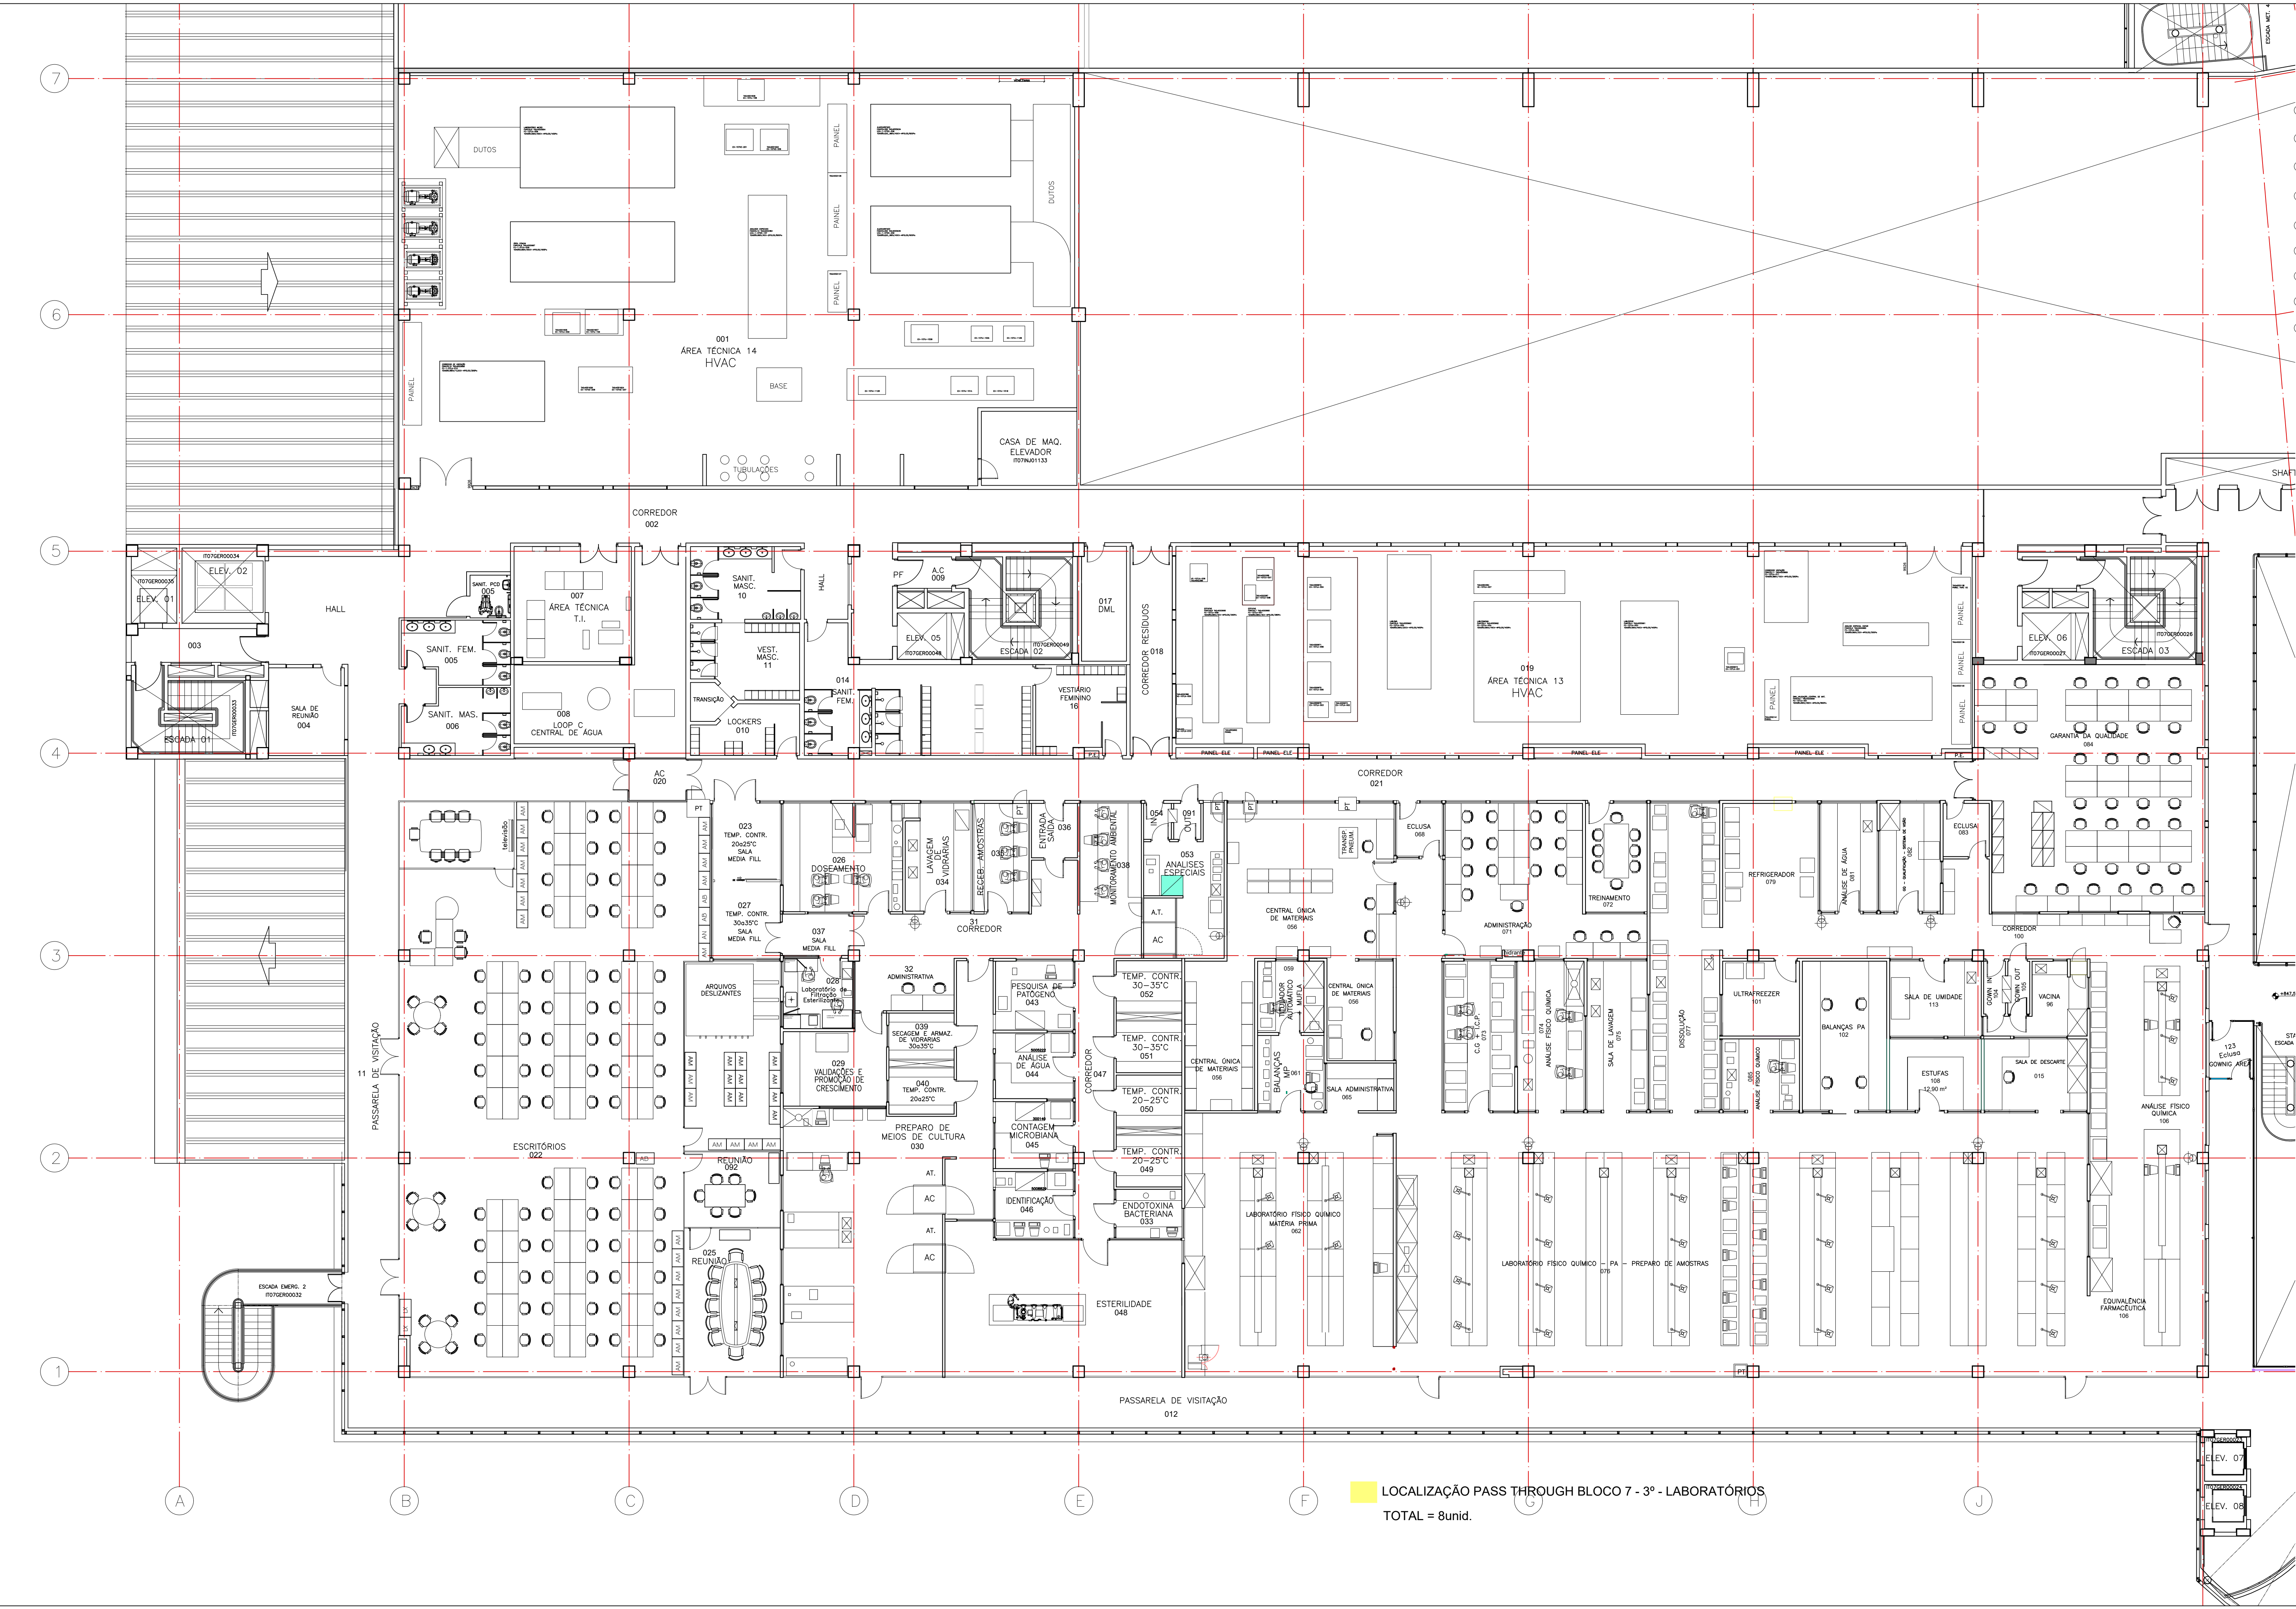

Rod. Castelo Branco Km 35,6 - Itapevi - SP.

Unidade: **ITAPEVI** Bloco: **BLOCO 7**

Etapa: **PROJETO AS BUILT**

Assunto: **BLOCO 7 - LABORATÓRIOS**
3º PAVIMENTO - LAYOUT PARCIAL

Escala:	1:125	Desenho:	EQ. ENG.ª					
Data:	09/2023	Projeto:	EQ. ENG.ª					
Arquivo:	08-07-FAR-ARQ-DE-00000-4300	Aprovado:	DIR. INDUSTRIAL					
Disciplina:								
UNID.	BLOCO	ÁREA	PROJETO	TIPO	Nº PROJETO	ETAPA	REV	ARQ
08	07	LAB	ARQ	DE	00000	4300	09	Folha:
								1/1

AVISO IMPORTANTE
Eurofarma. Todos os direitos reservados.
A reprodução de qualquer parte desta obra, por qualquer meio, somente é permitida com o consentimento por escrito da Eurofarma.